

GENERAL NOTESSHEET INDEX

T1 TITLE SHEET
SP1 SITE PLAN
A1 FLOOR PLAN
A2 ELEVATION
A3 ELEVATION
A4 BLDG. SECTION
A5 WALL & DETAIL
SECTION

AMY
CHANTITLE SHEET

002-445-01
1160 PACIFIC ST.
SAN LUIS OBISPO, CA

KARL
KUNDERT

MARCH
20, 08

T1
ARCH 24 2
COMBRINK

GENERAL NOTES

1. PROPERTY LINE
2. CREEK LINE
3. SIDEWALK
4. PATIO

AMY
CHAN


KUNDER
MEDICAL
CLINIC ADDITION

002-448-01
1160 PACIFIC ST
SAN LUIS OBISPO, CA

KARL
KUNDER

MARCH
20, 08


SPI
MARCH 24 2
COMBINEK

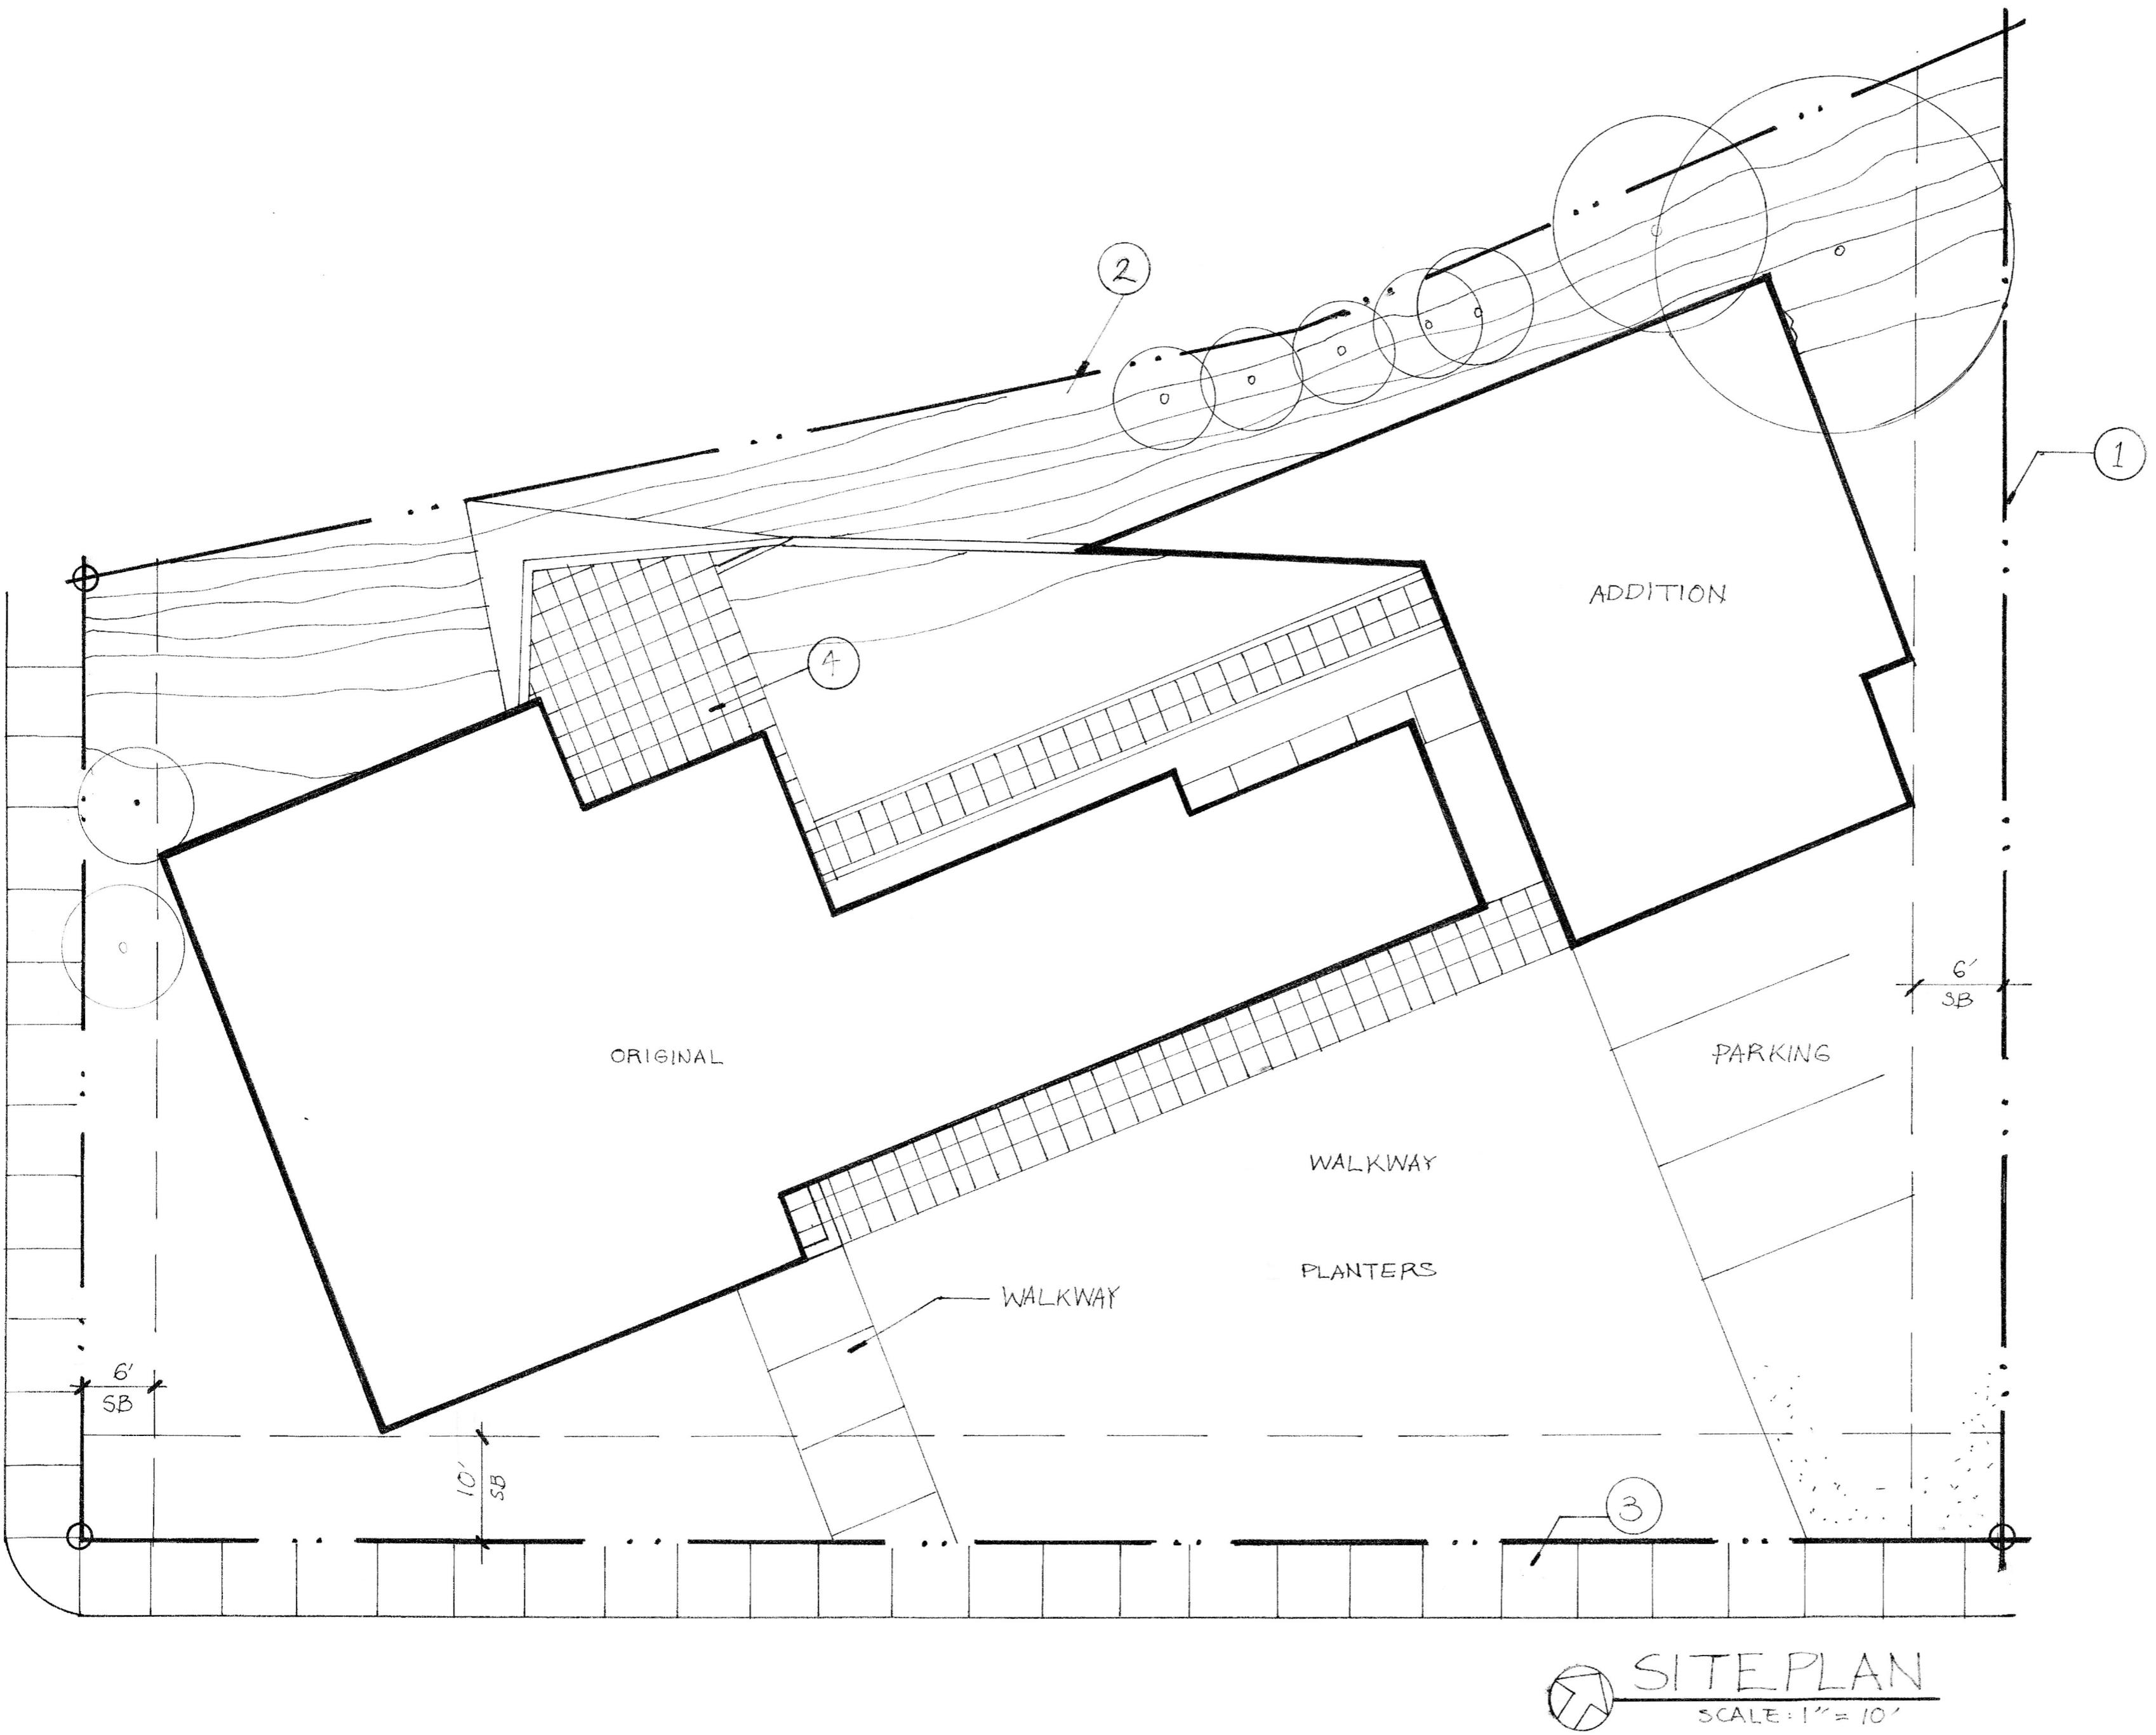

FLOOR PLAN KEYNOTE

1. OVERHANG
2. BULLETIN DESK
3. COLONNADE WALKWAY - WOOD POST 8x8"

AMY
CHAN

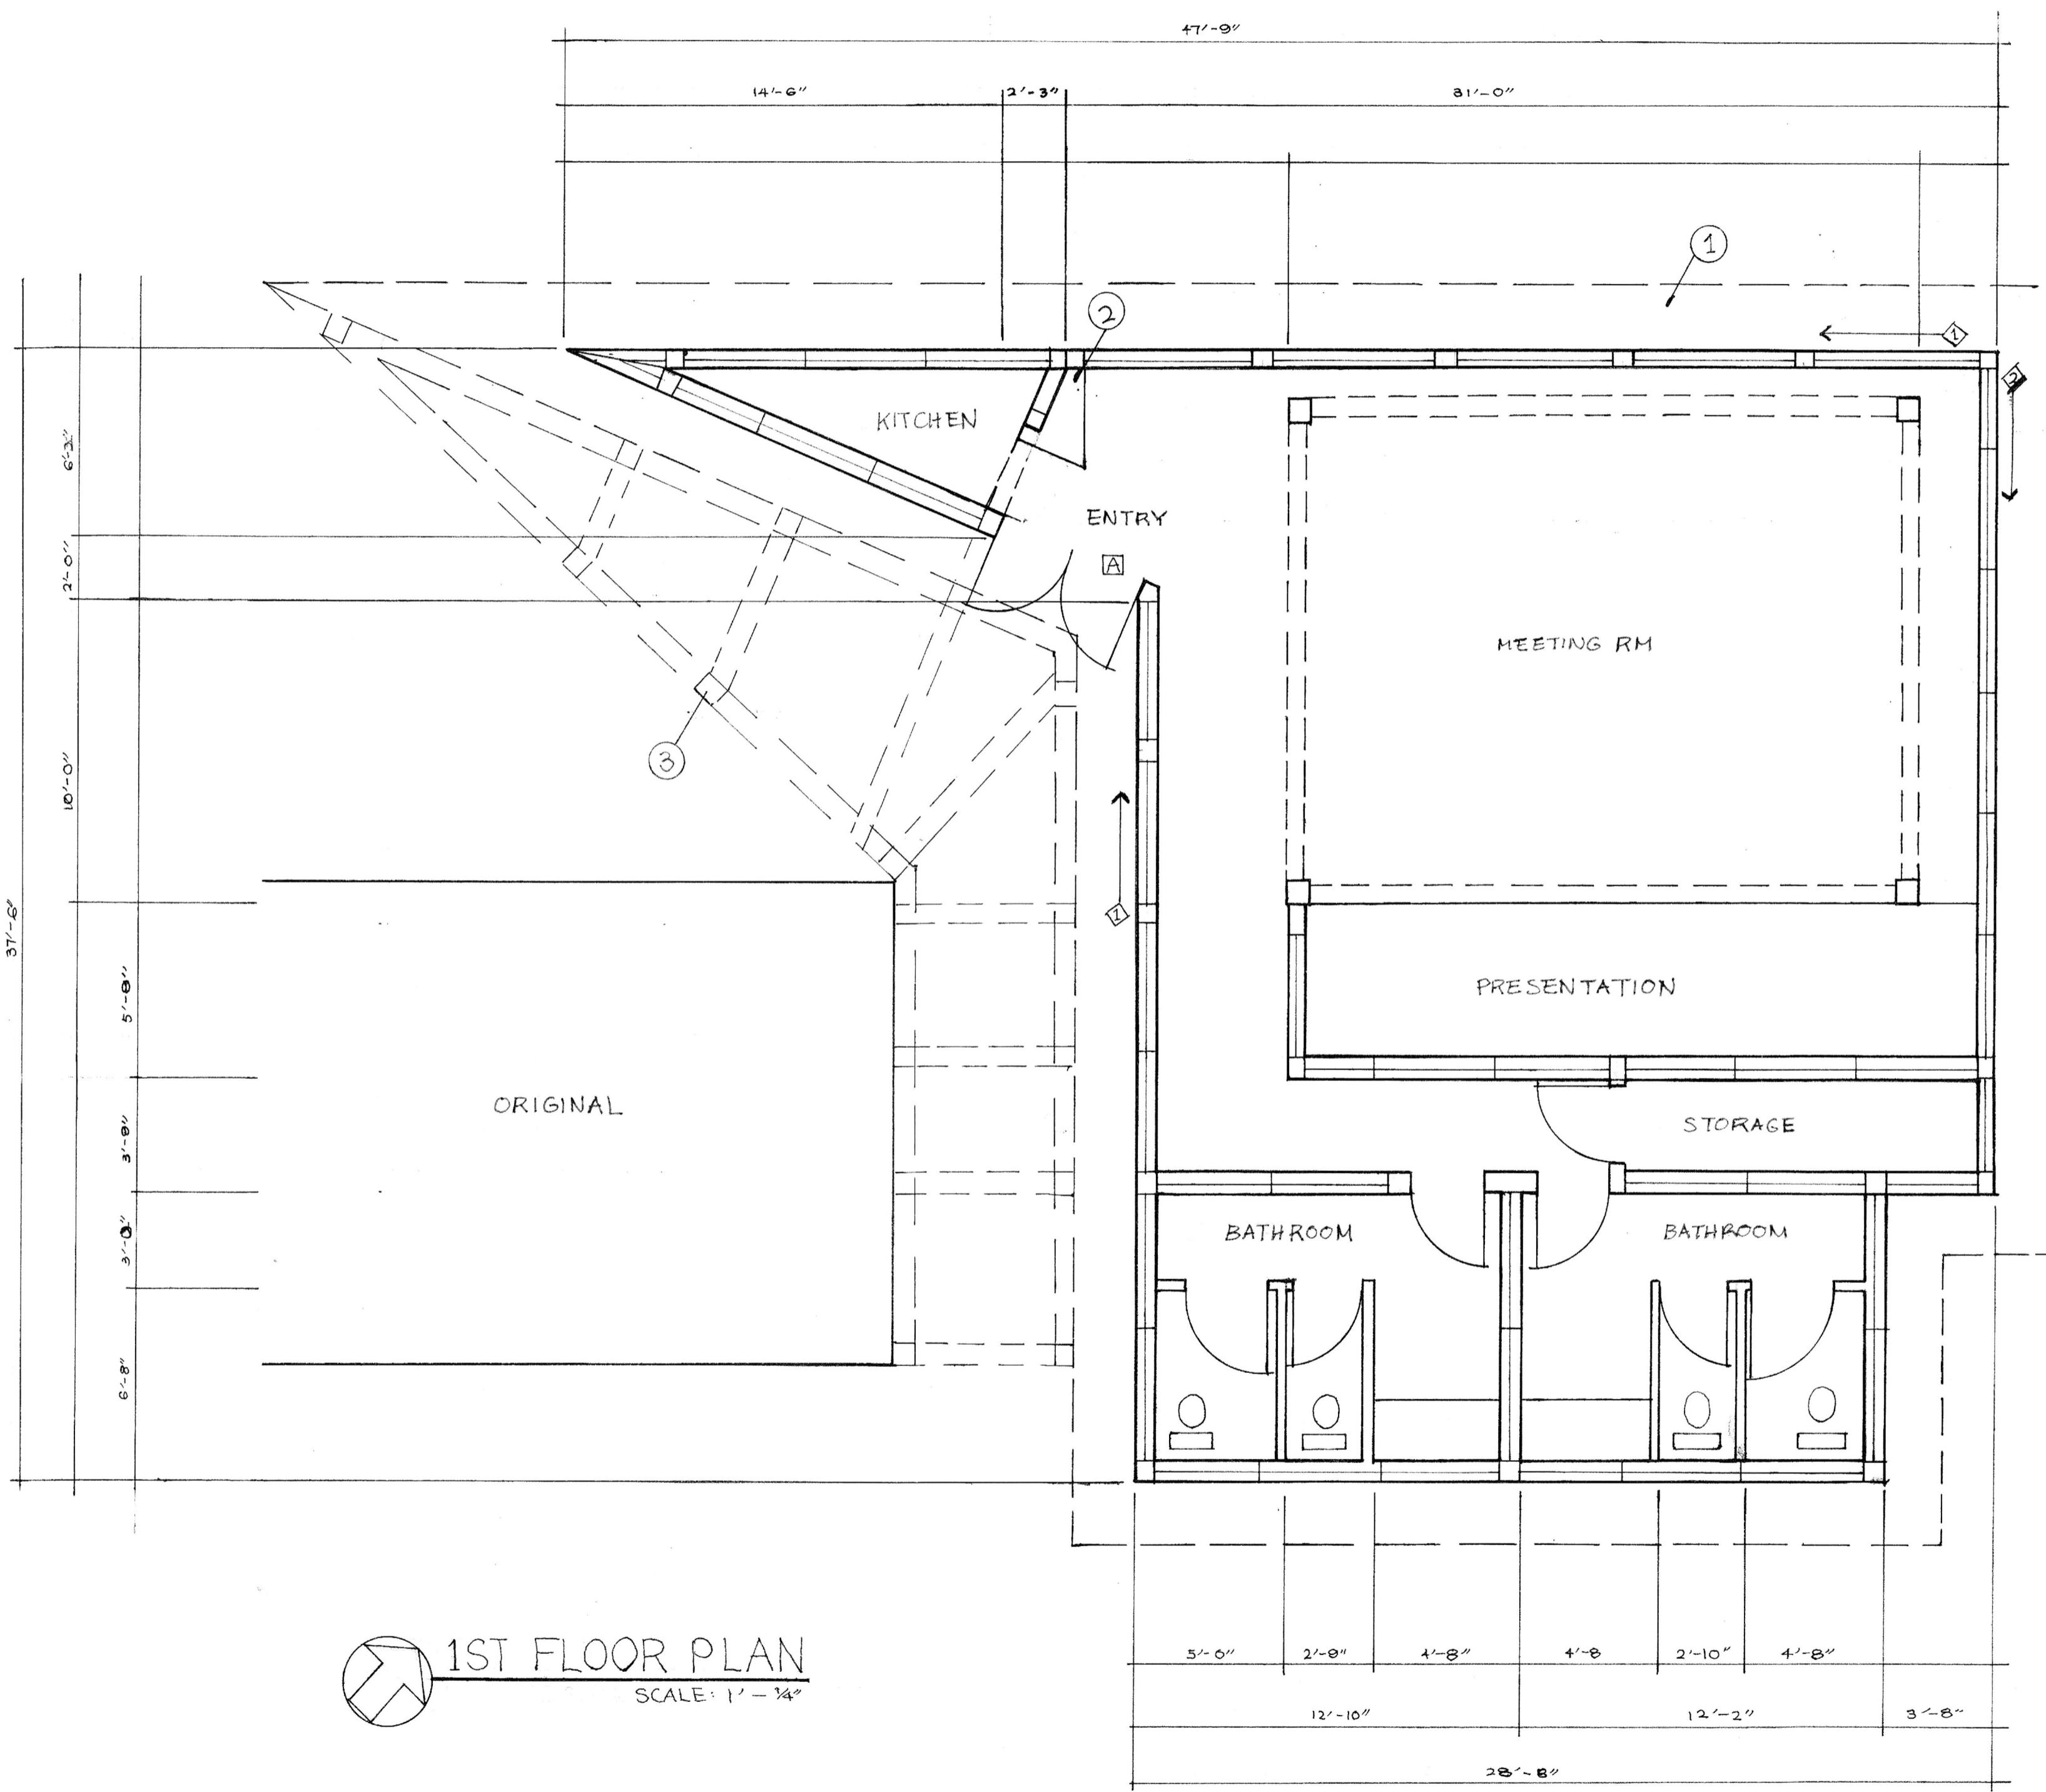

DOOR/WINDOW

- ◊ WINDOW - TRANSLUCENT PANELS
- ◊ WINDOW - CLEAR GLASS WALL
- WOOD FRAME GLASS DOOR

002-445-01
1160 PACIFIC ST.
SAN LOIS OBISPO, CA

KARL
KUNDERT

MARCH
20, 08

A.I.
ARCH 242
COMBRINK


KUNDERT
MEDICAL
CLINIC ADDITION

ELEVATION KEYNOTES.

1. ROOF-METAL ROOF - STANDING SEAM
2. WOOD FASCIA (CONT.)
3. CELESTORY
4. FIREPLACE CHIMNEY AND FLUE
- 5.
- 6.
7. WALLS - "NEW BRICK"
8. CONC. BULKHEAD
- 9.
- 10.
11. CONC. STAIR
- 12.
13. WINDOWS - TRANSLUCENT
WINDOW PANELS W/ WOOD DESIGN
- 14.
- 15.
- 16.
17. DOORS - WOOD/ GLASS PANEL
- 18.
- 19.
- 20.


AMY
CHAN

KUNDERT
MEDICAL
CLINIC ADDITION

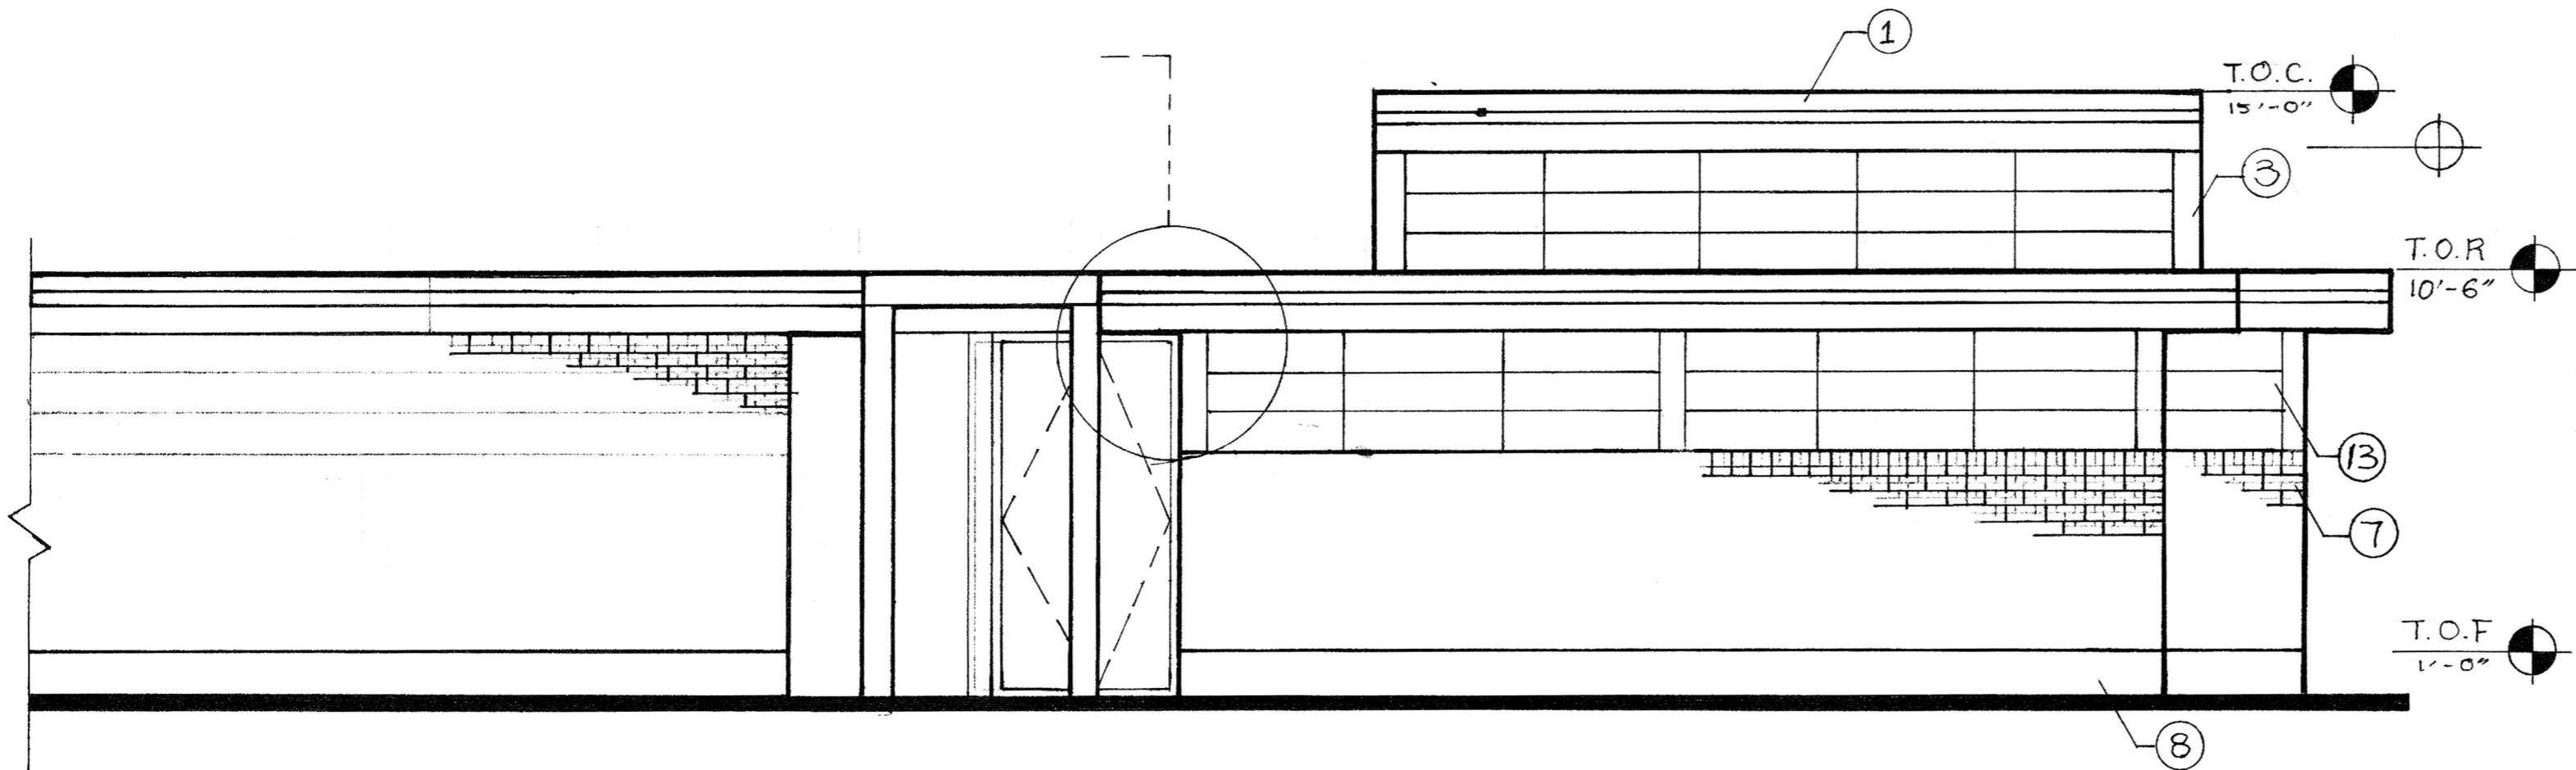

NORTH ELEVATION

SCALE: 1'-1/4"

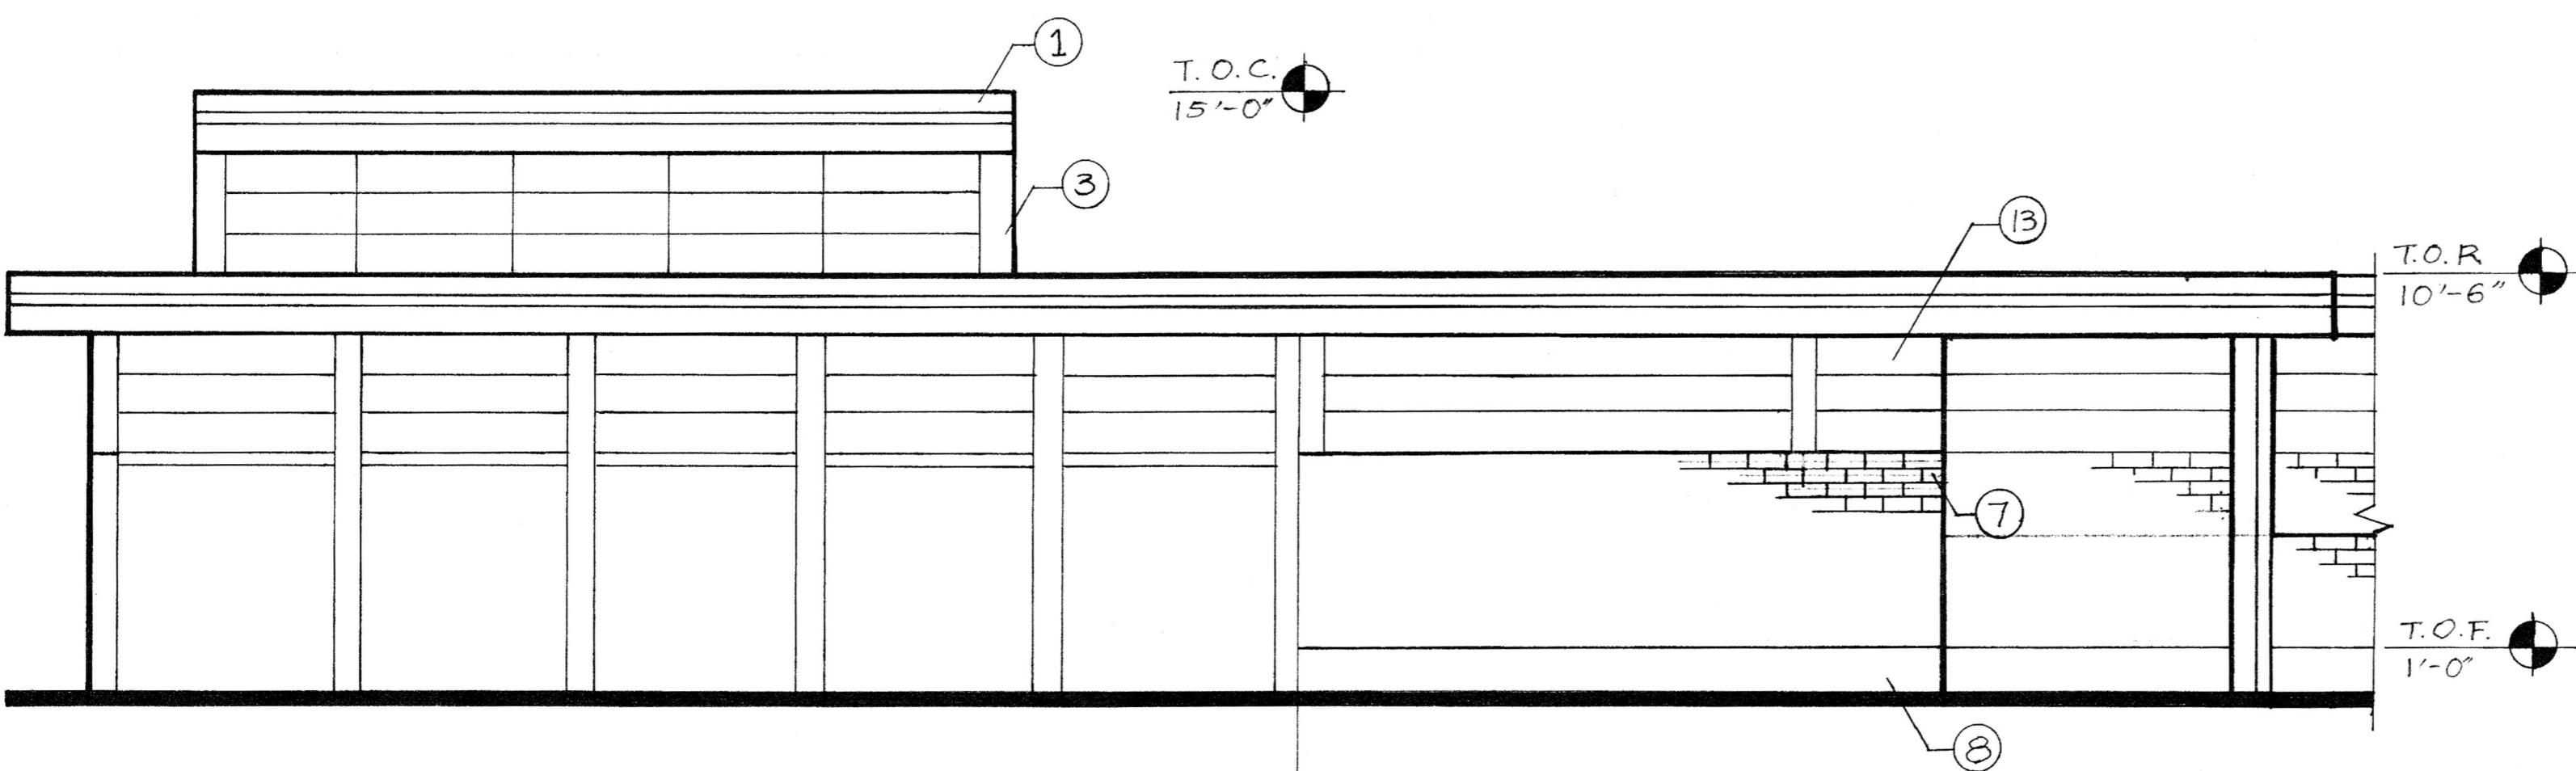

SOUTH ELEVATION

SCALE: 1'-1/4"

002-445-01
1160 PACIFIC ST.
SAN LUIS OBISPO, CA

KARL
KUNDERT

MARCH
20, 08


A2
ARCH 242
COMBRICK

ELEVATION KEYNOTES

1. ROOF - METAL ROOF - STANDING SEAM
2. WOOD FASCIA (CONT.)
3. CELESTORY
4. FIREPLACE CHIMNEY AND FLUE
- 5.
- 6.
7. WALLS - "NEW BRICK"
8. CONC. BULKHEAD
- 9.
- 10.
11. CONC. STAIR
- 12.
13. WINDOWS - TRANSLUCENT
WINDOW PANELS W/ WOOD DESIGN
14. WINDOWS - CLEAR GLASS WALL
- 15.
- 16.
17. DOORS - WOOD / GLASS PANEL


AMY
CHAN

KUNDERT
MEDICAL
CLINIC ADDITION

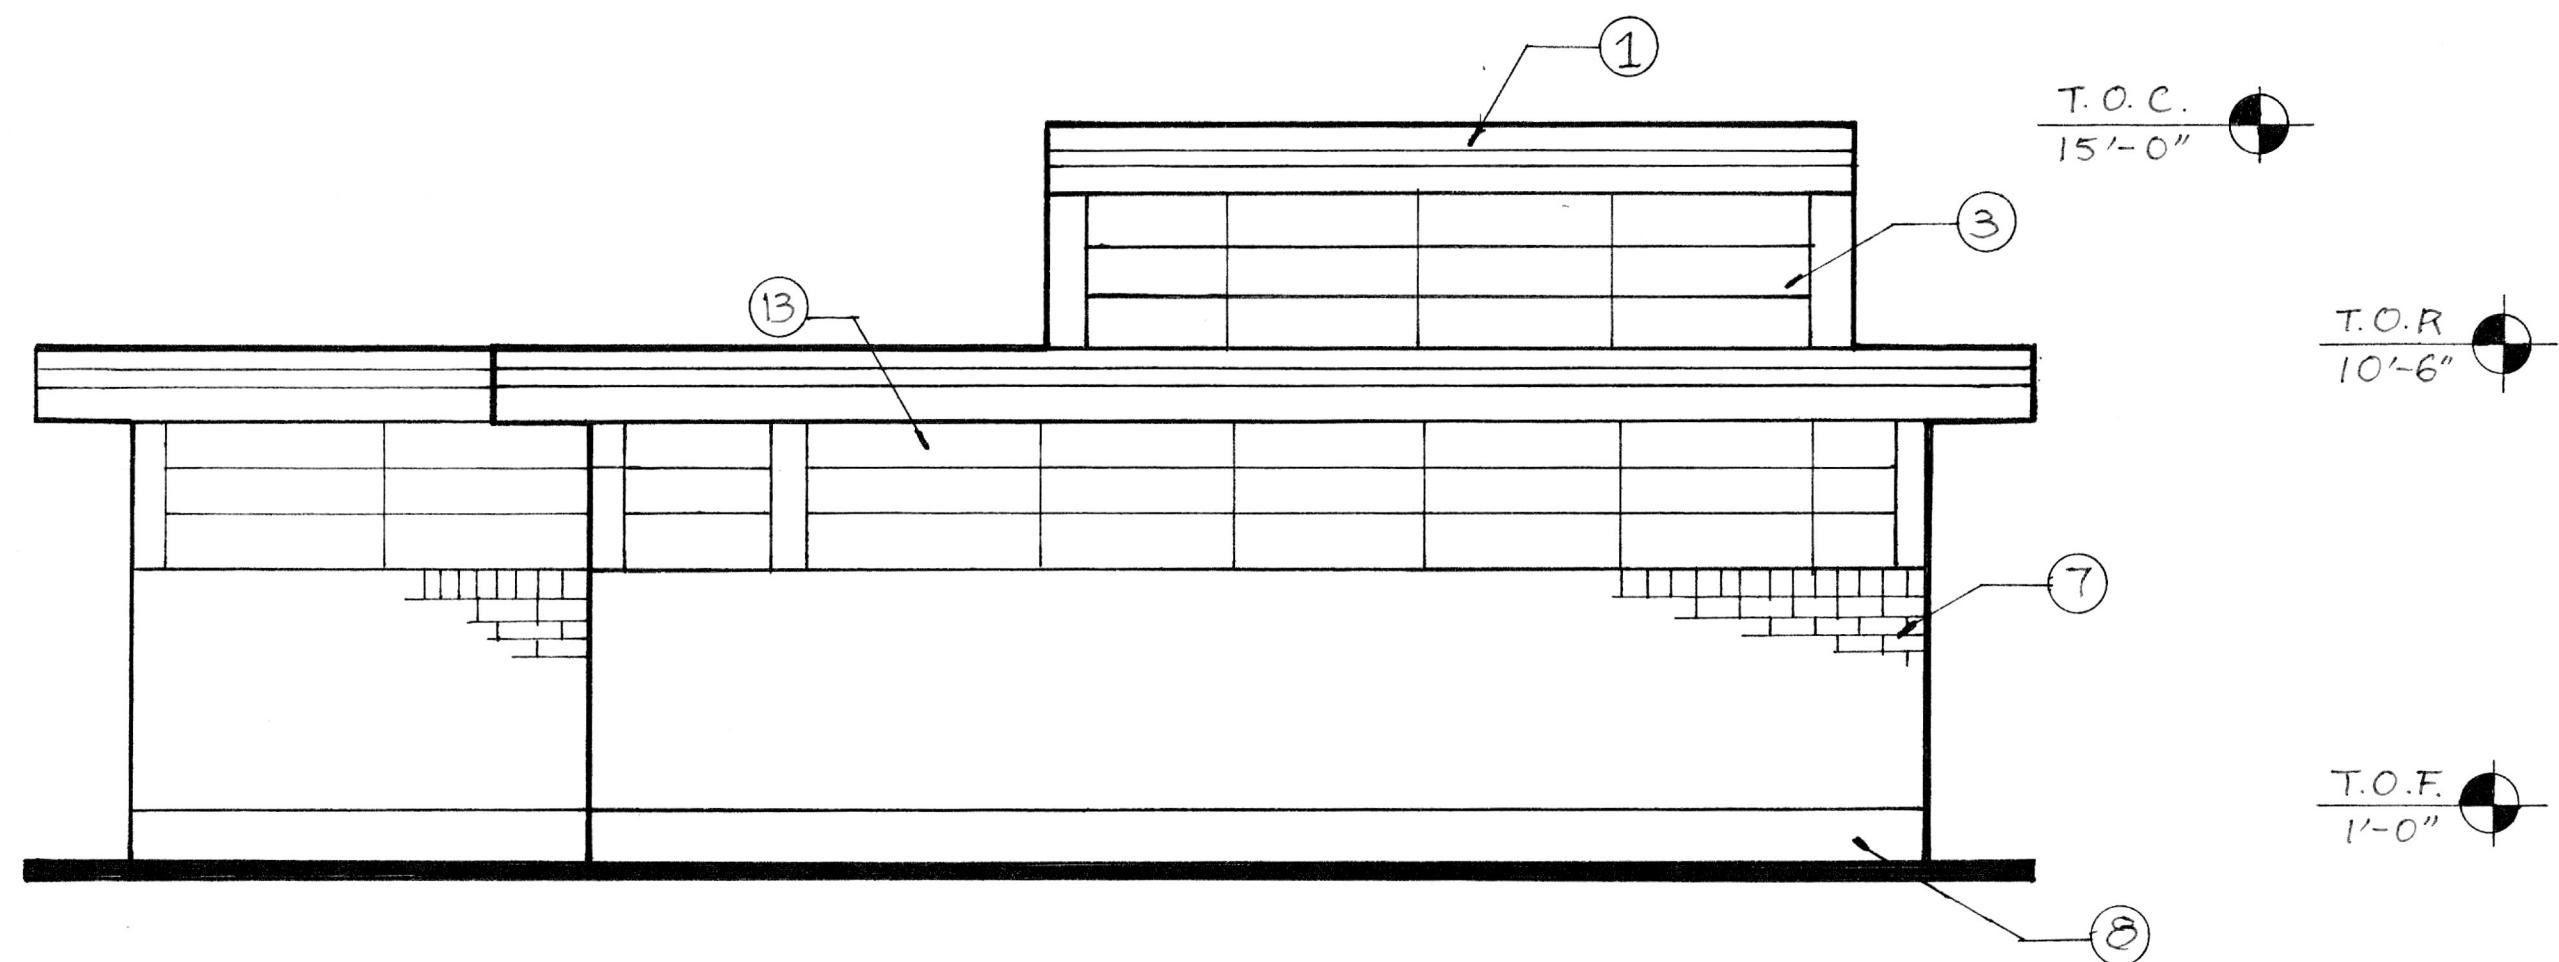

EAST ELEVATION

SCALE: 1'-1/4"

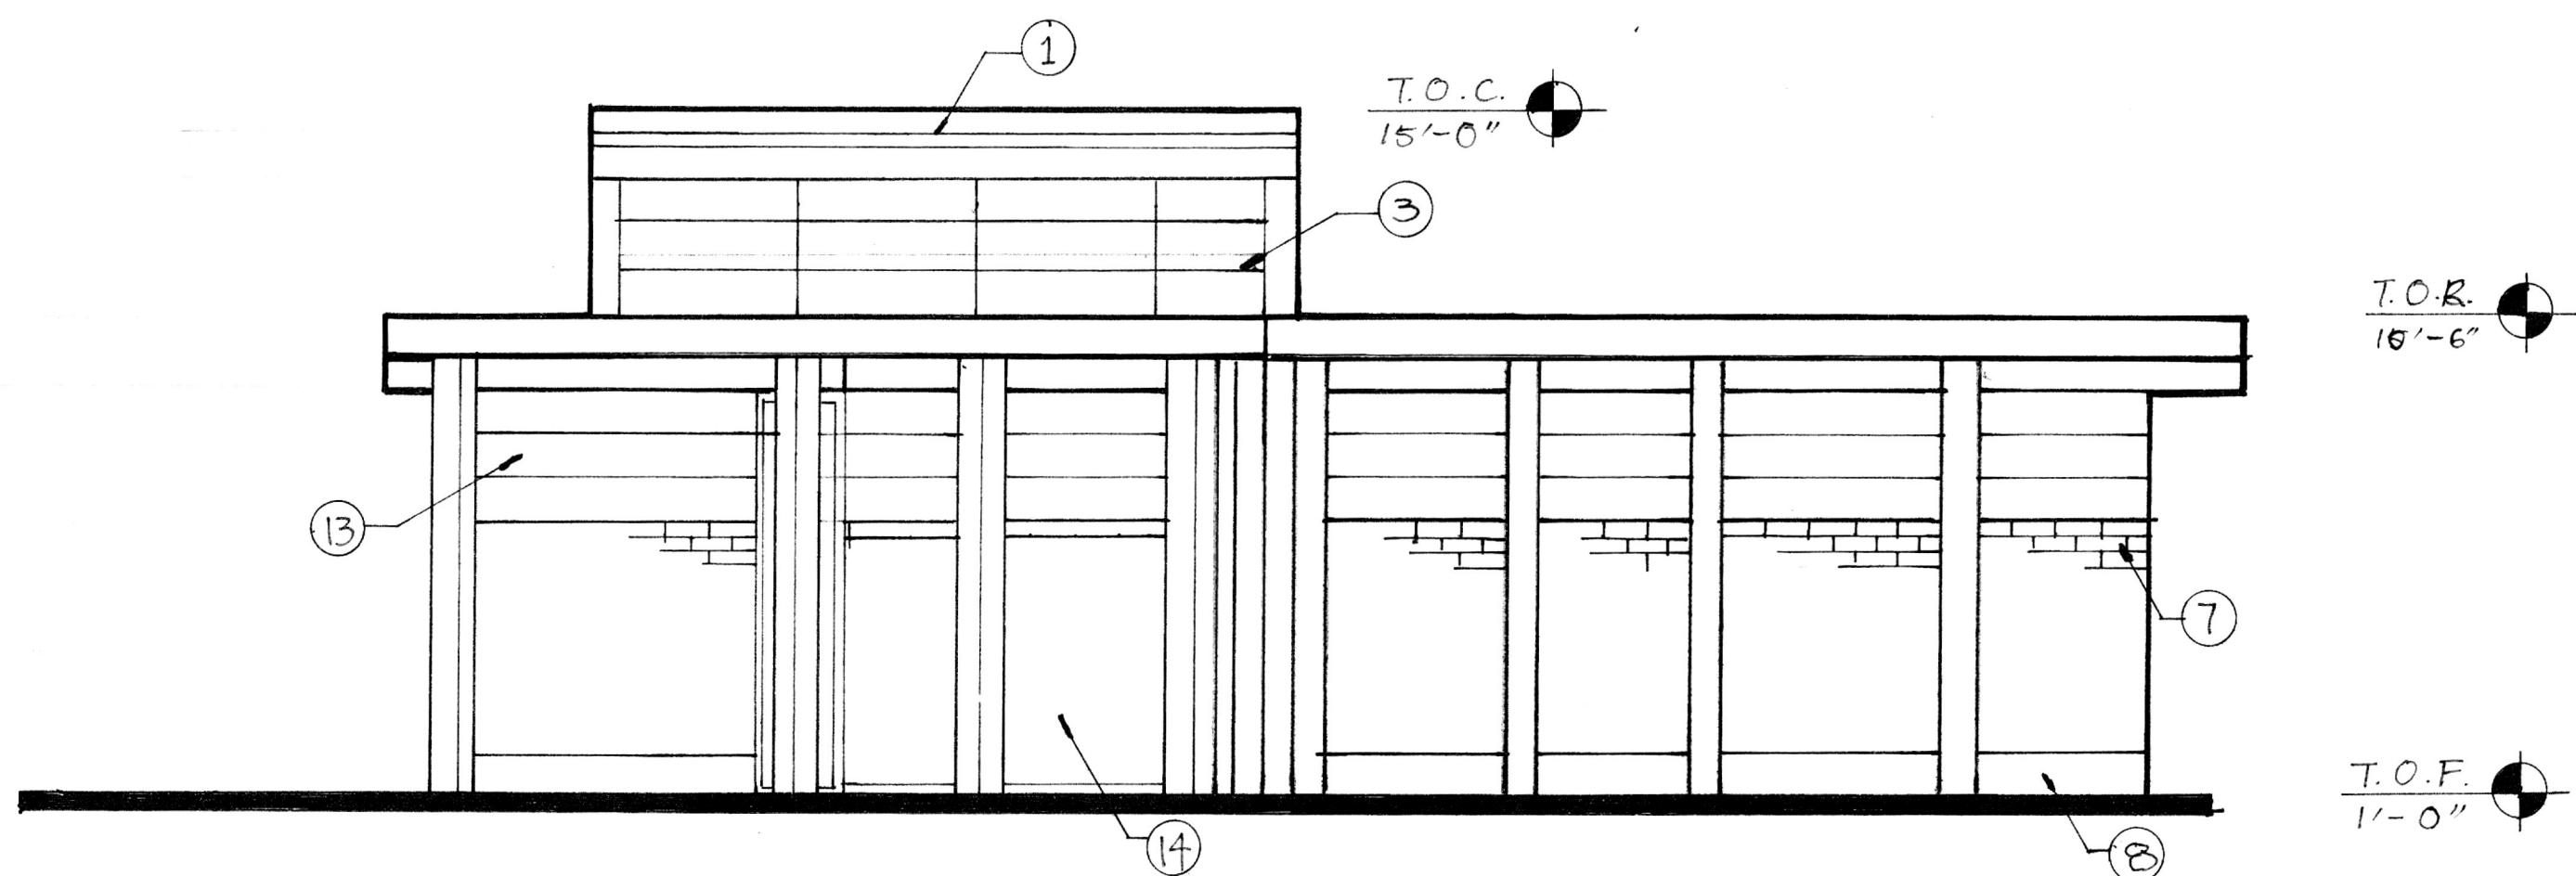

WEST ELEVATION





SCALE: 1'-1/4"

002-445-01
1180 PACIFIC ST.
SAN LUIS OBISPO, CA

KARL
KUNDERT

MARCH
20, 08

A3
ARCH 242
COMBRINK

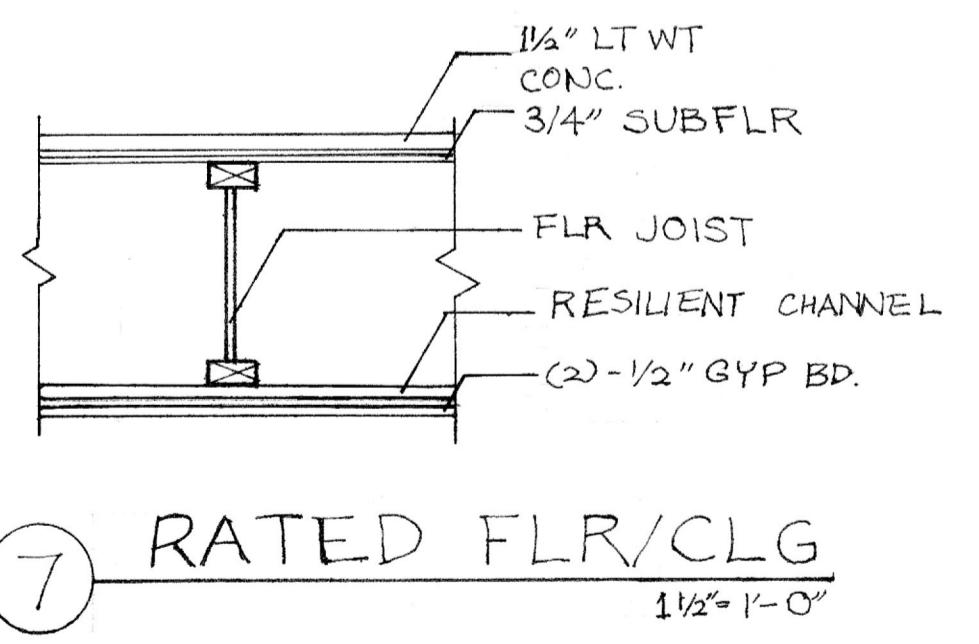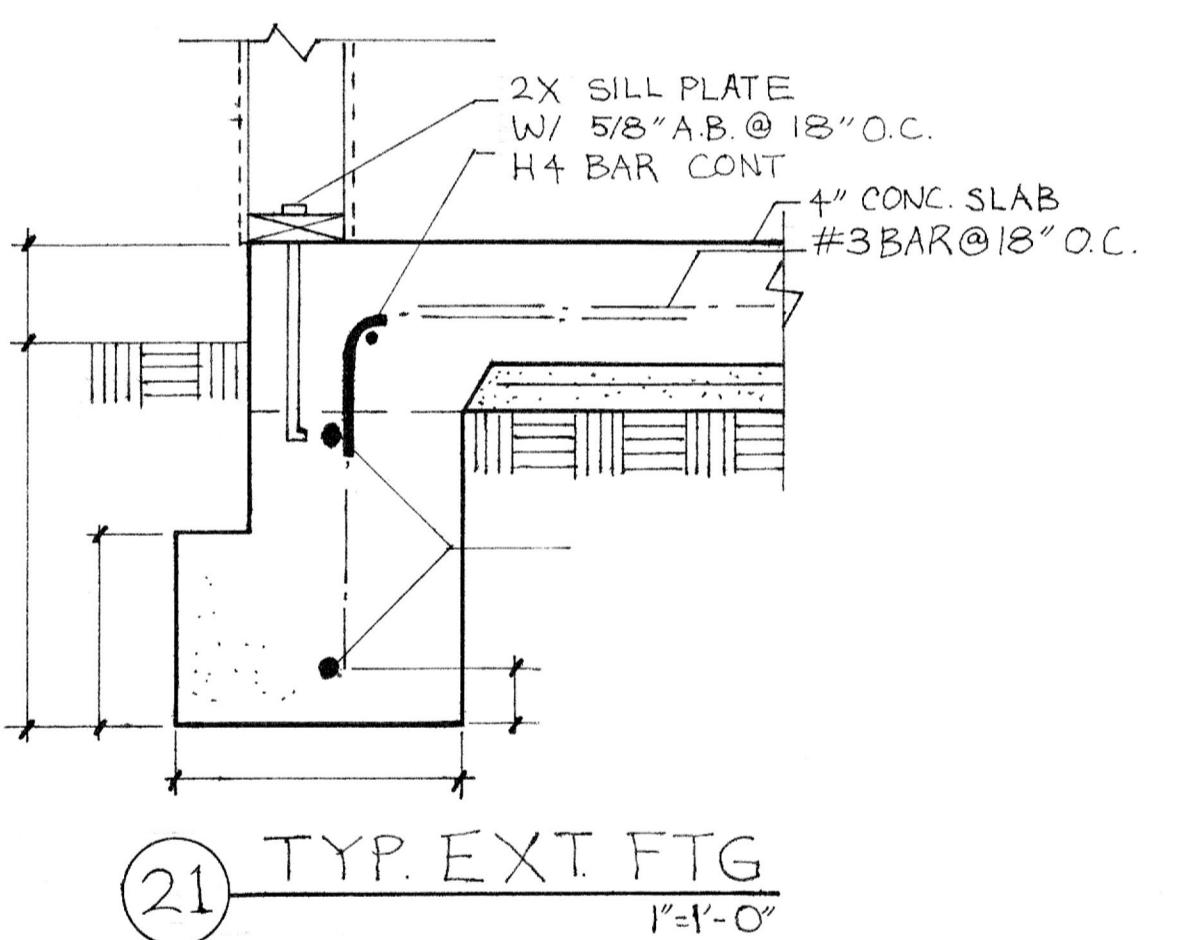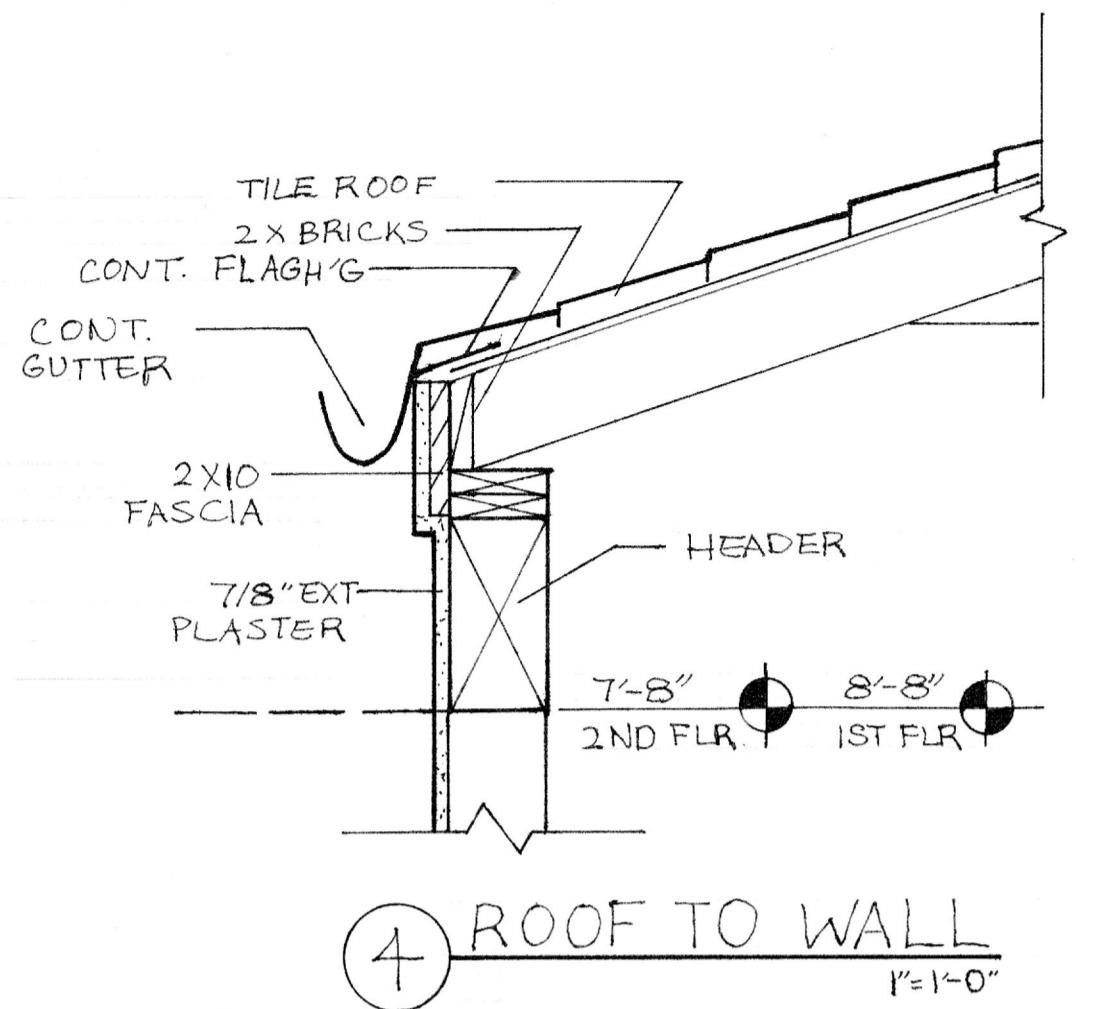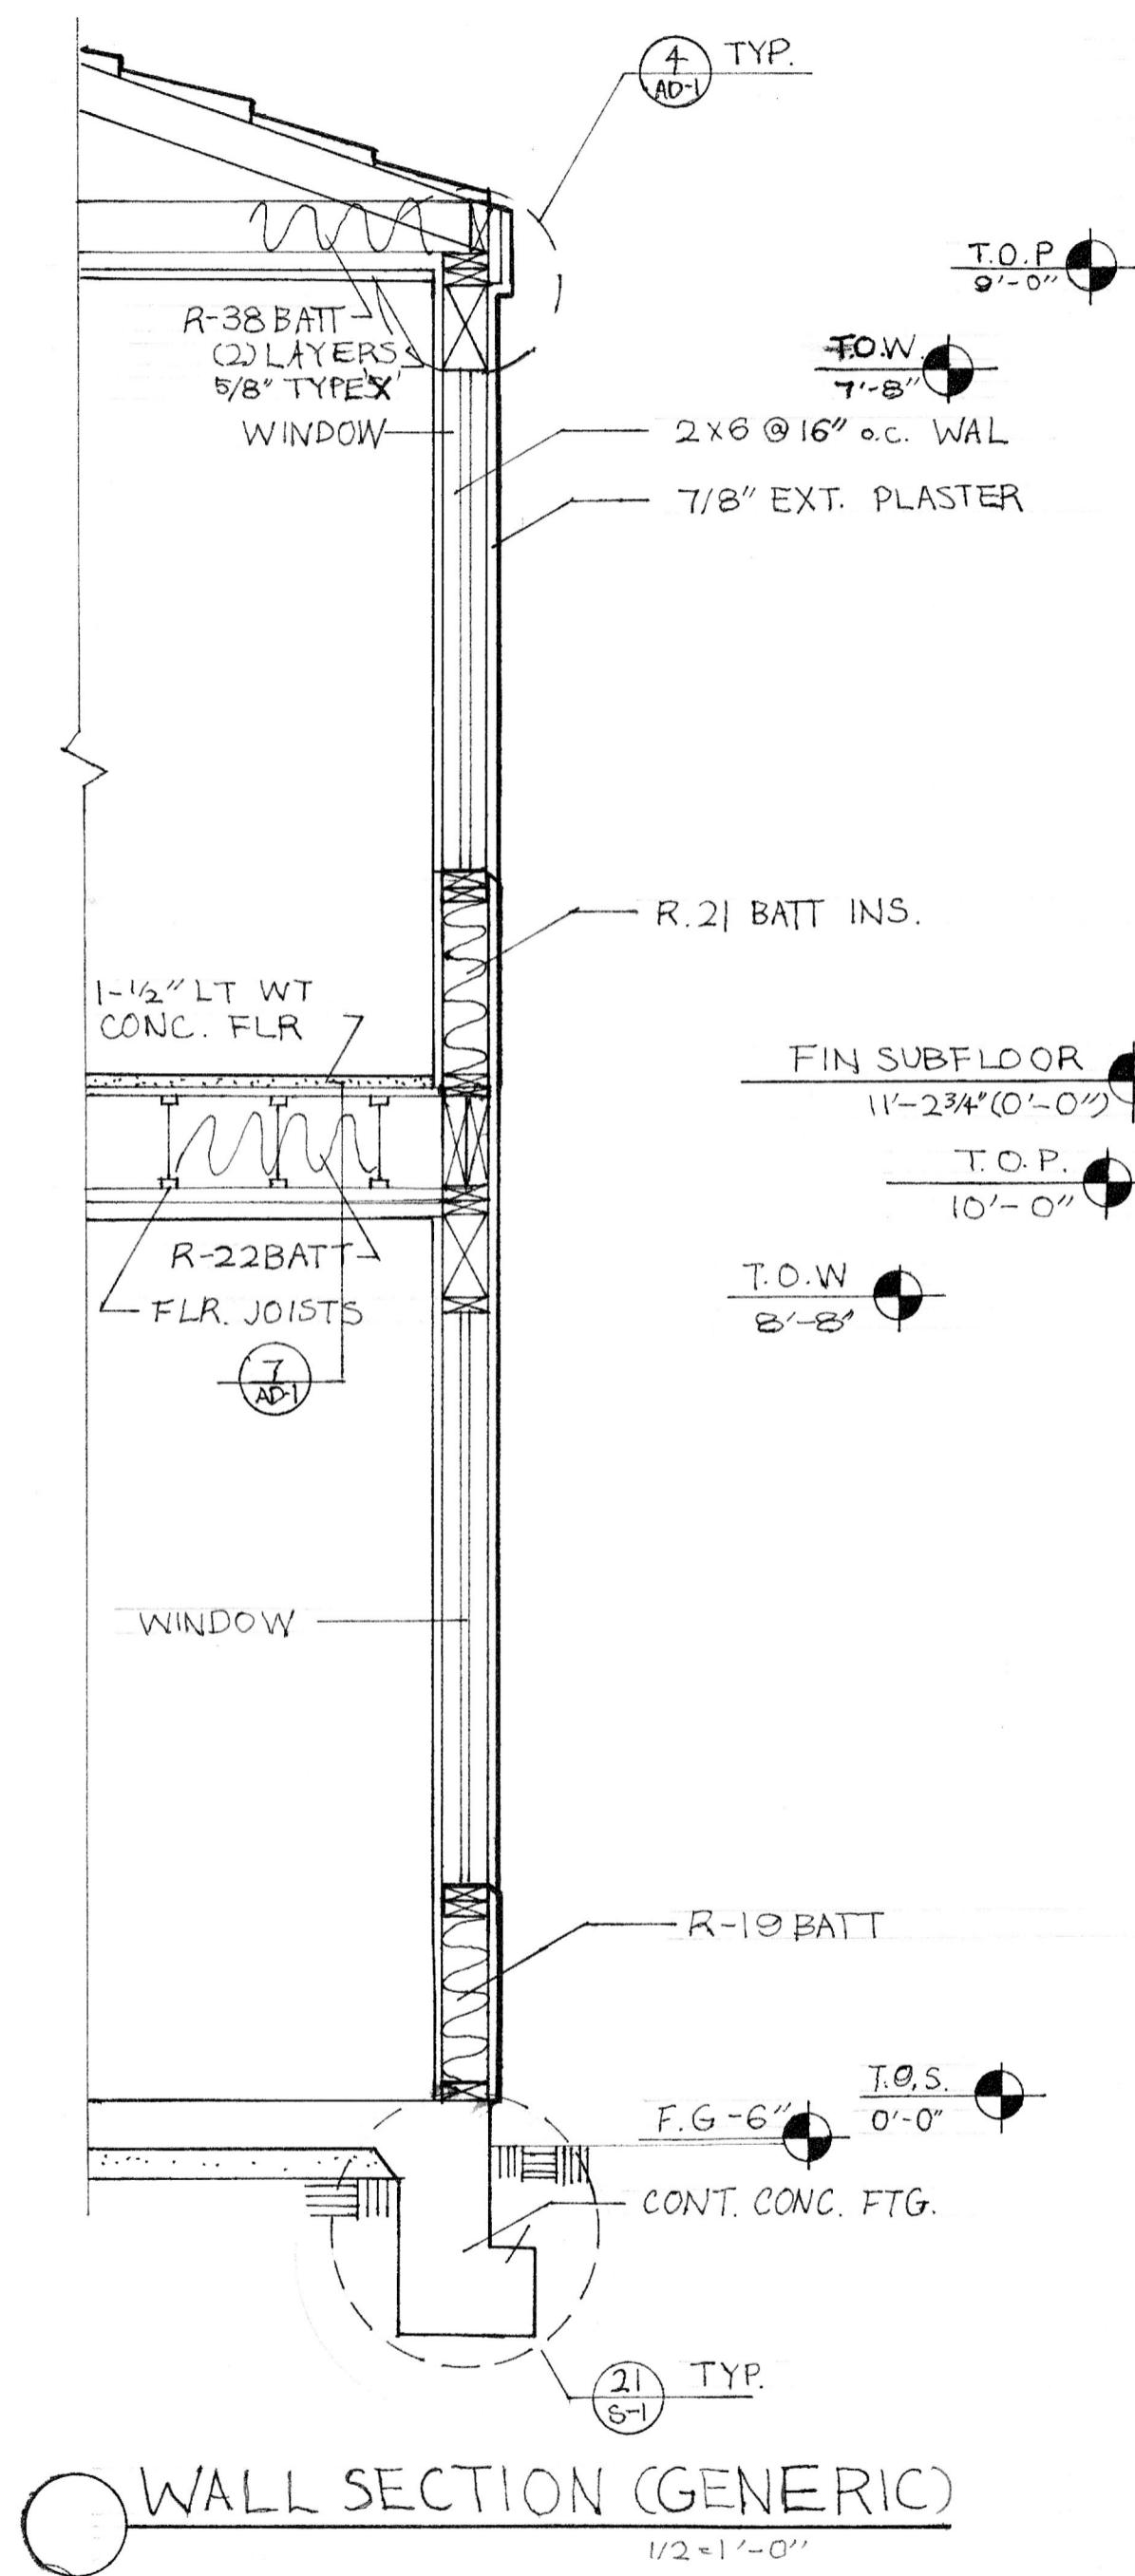

SECTION KEYNOTES

1. ROOF-METAL ROOF-STANDING SEAM
2. CELESTORY
3. WALLS "NEW BRICK"
4. CONCRETE BULKHEAD
5. WINDOWS-TRANSLUCENT WINDOW PANEL W/ WOOD DESIGN
6. WINDOWS-CLEAR GLASS CURTAIN WALL
7. WOOD POST-8"x8"
8. INSULATION-2'x12" O.C.

AMY
CHAN


KUNDERT
MEDICAL
CLINIC ADDITION

002-445-011
1160 PACIFIC ST.
SAN LUIS OBISPO, CA

KARL
KUNDERT

MARCH
20, 08

A 5
ARCH 242
COMBRINK

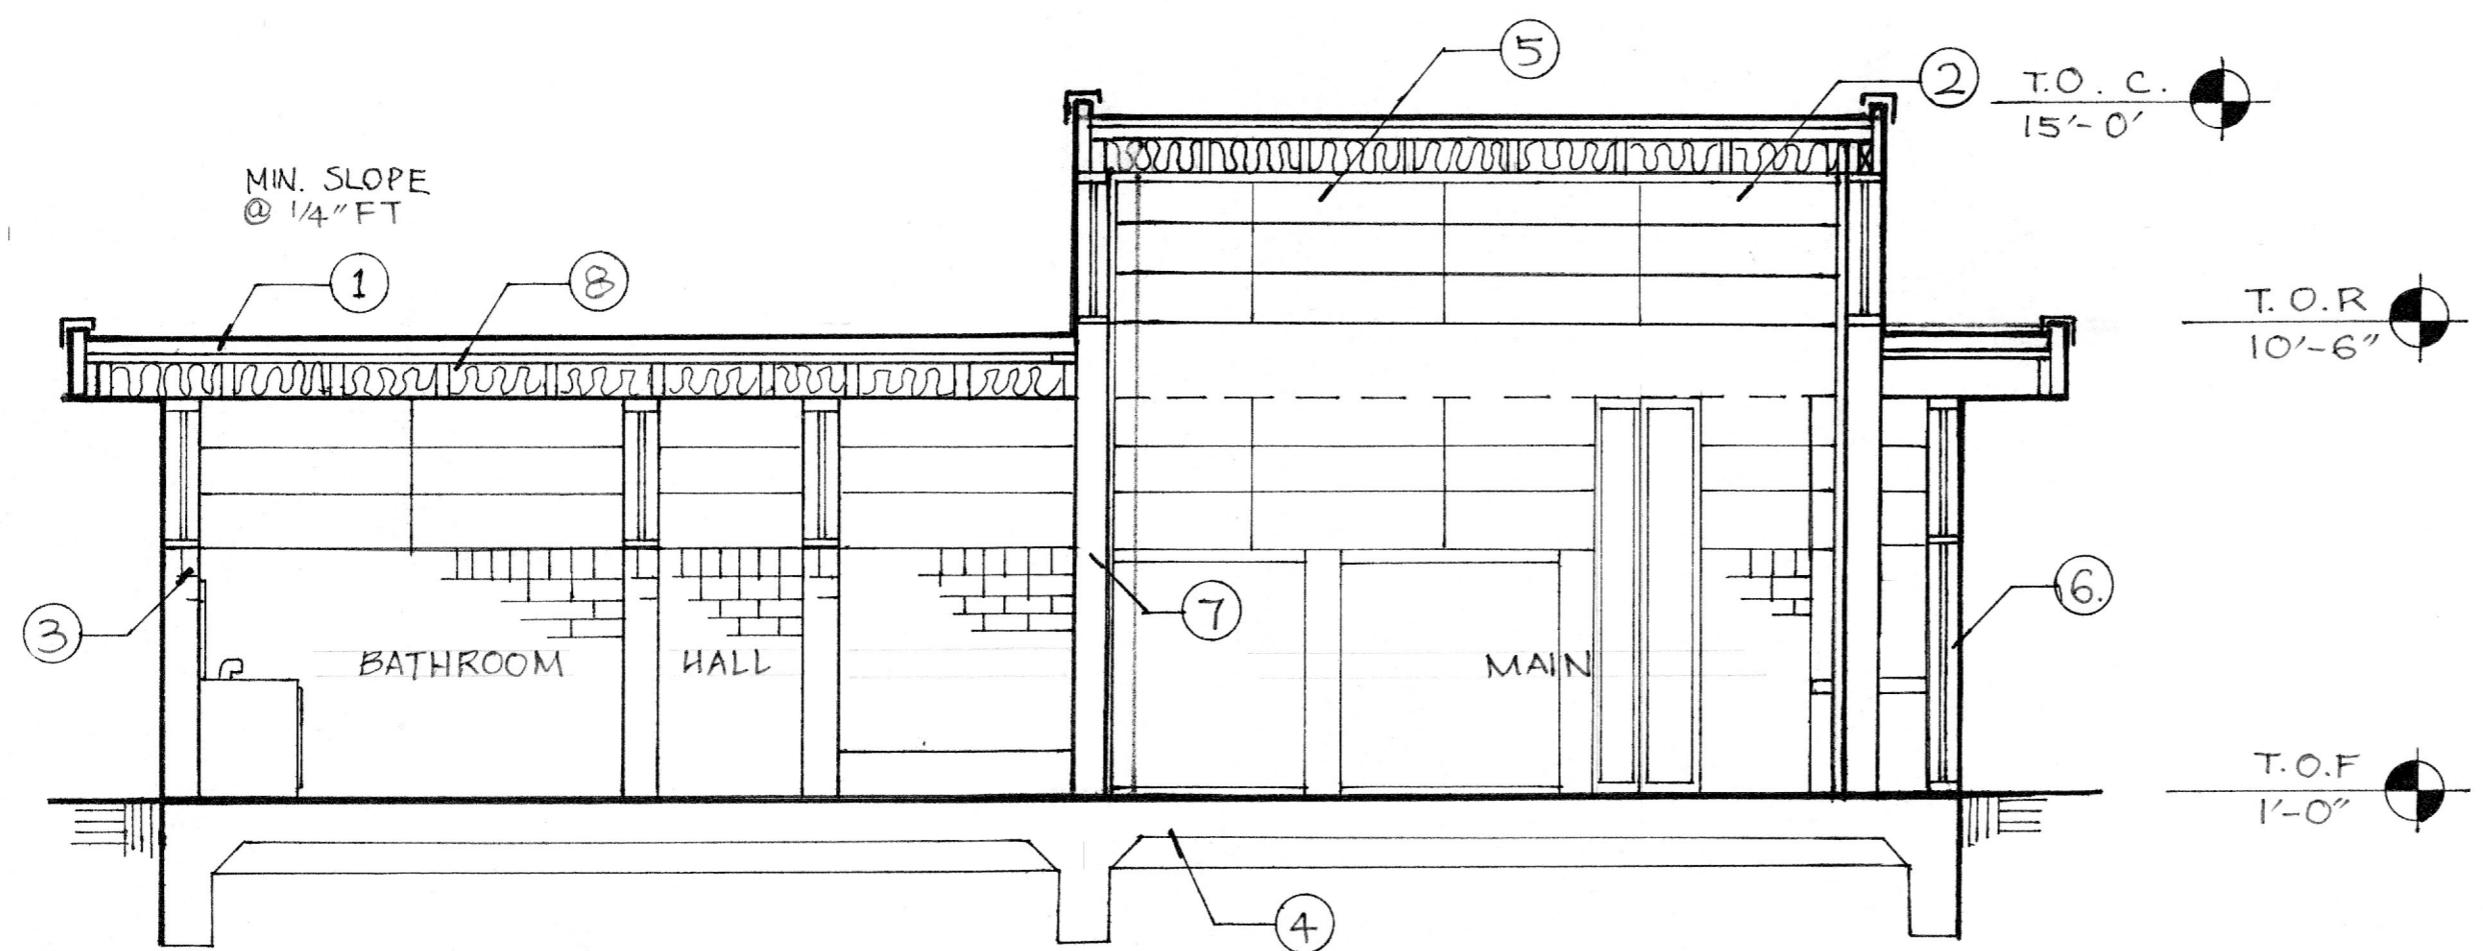

BLDG SECTION

SCALE: 1"- 1/4"